Calle Macarena · cotejo visual V2

Planta definitiva con trastero · modelo 1:1 · geometría de los meshes reales

Este documento no hereda ningún resultado APTO ni la cuenta de controles de V1. El resultado numérico V2 debe evaluarse por separado antes de los renders fotográficos.

Planta: página1 izquierda del PDF definitivo, registrada +112,68 pt en X, escala nominal fija 1:150 = 0,05291666666666667 m/pt. Una cota escrita prevalece sobre su pequeño residual gráfico; por ello el contorno medido no se deforma para ocultar diferencias del dibujo.

Alzados y secciones: páginas38 y39 del básico. Comparan la geometría existente. La antigua pérgola se sustituye por el trastero del plano final: el volumen nuevo no puede coincidir con las vistas antiguas en ese ámbito.


Trastero: inferior/superior del forjado 3,35/3,70 m, coronación de peto 4,40 m, puerta norte 2,03 m y portón frontal 2,50 m son confirmaciones expresas del usuario V2. Estas alturas no están escritas en el PDF definitivo.

Persisten datos no definidos: profundidad/fondo de piscina, niveles reales de agua y peldaños, mecanismo y despiece del portón, capas/pendientes de cubierta y cielorraso del trastero. Mobiliario, vehículos, vegetación, materiales y luminarias son visualización.

```
Identidad del modelo: SHA256 fb95f5a917521943a95156dddfd34bc930952a3da4e8c00ac8ab4f6ad999a1f0
```


Mediciones revisión V2; documento generado 2026-10-07 07:30 UTC

Planta del mesh y superposición con el plano definitivo

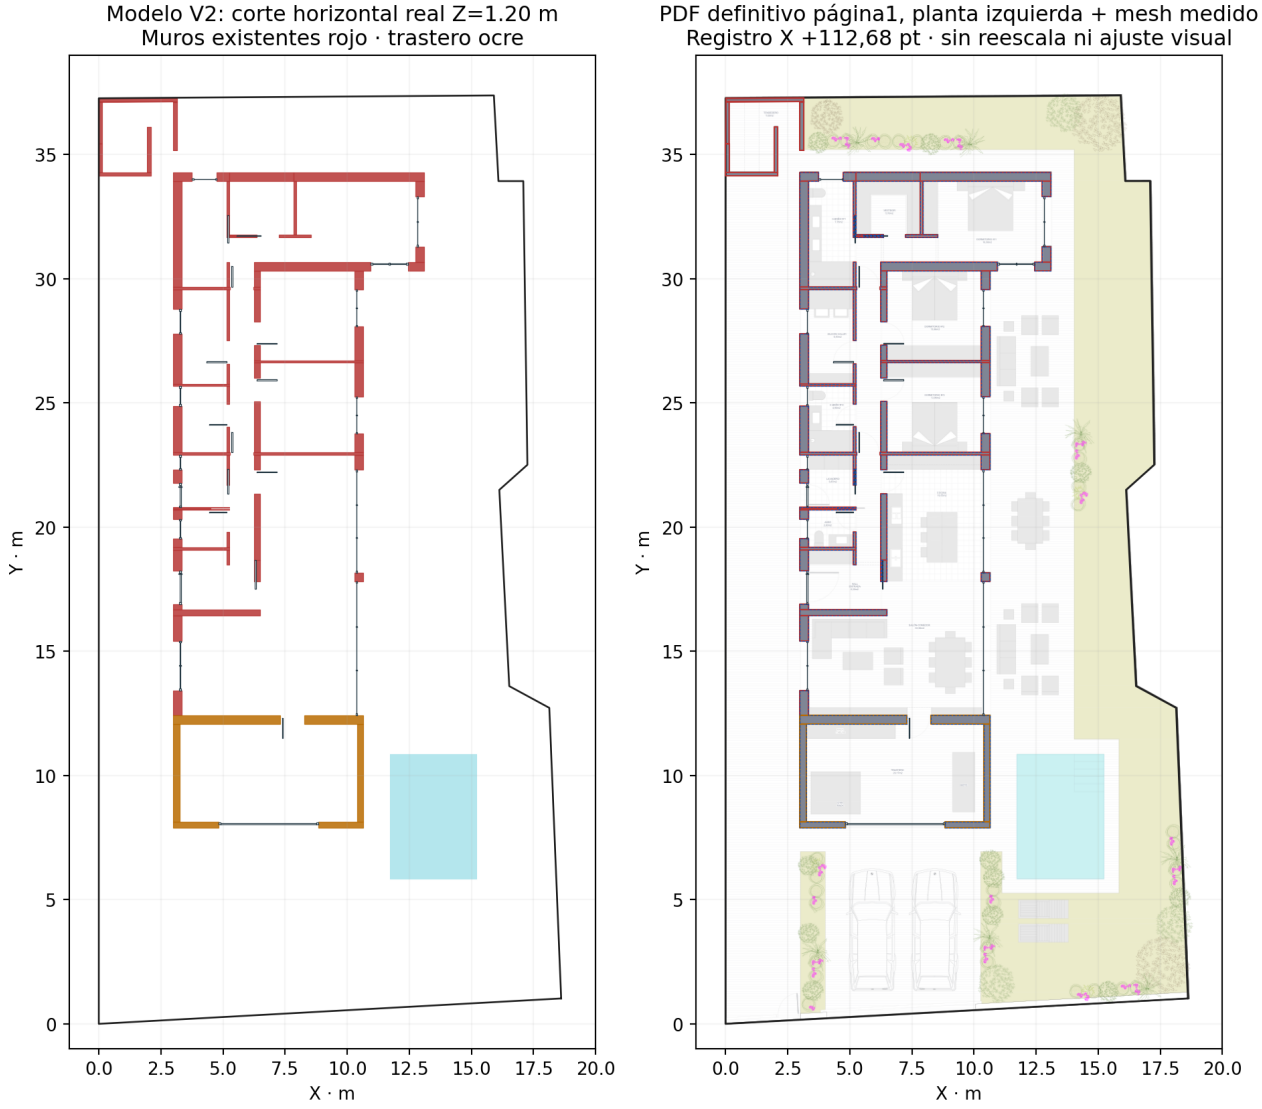


La cota directa prevalece sobre residuos gráficos. Líneas azules: rellenos del PDF; rojo/ocre: mesh.
El cerramiento parcelario aquí se muestra por su lindero documental; las ortográficas 3D están en hojas separadas.

Alzado · puerta principal

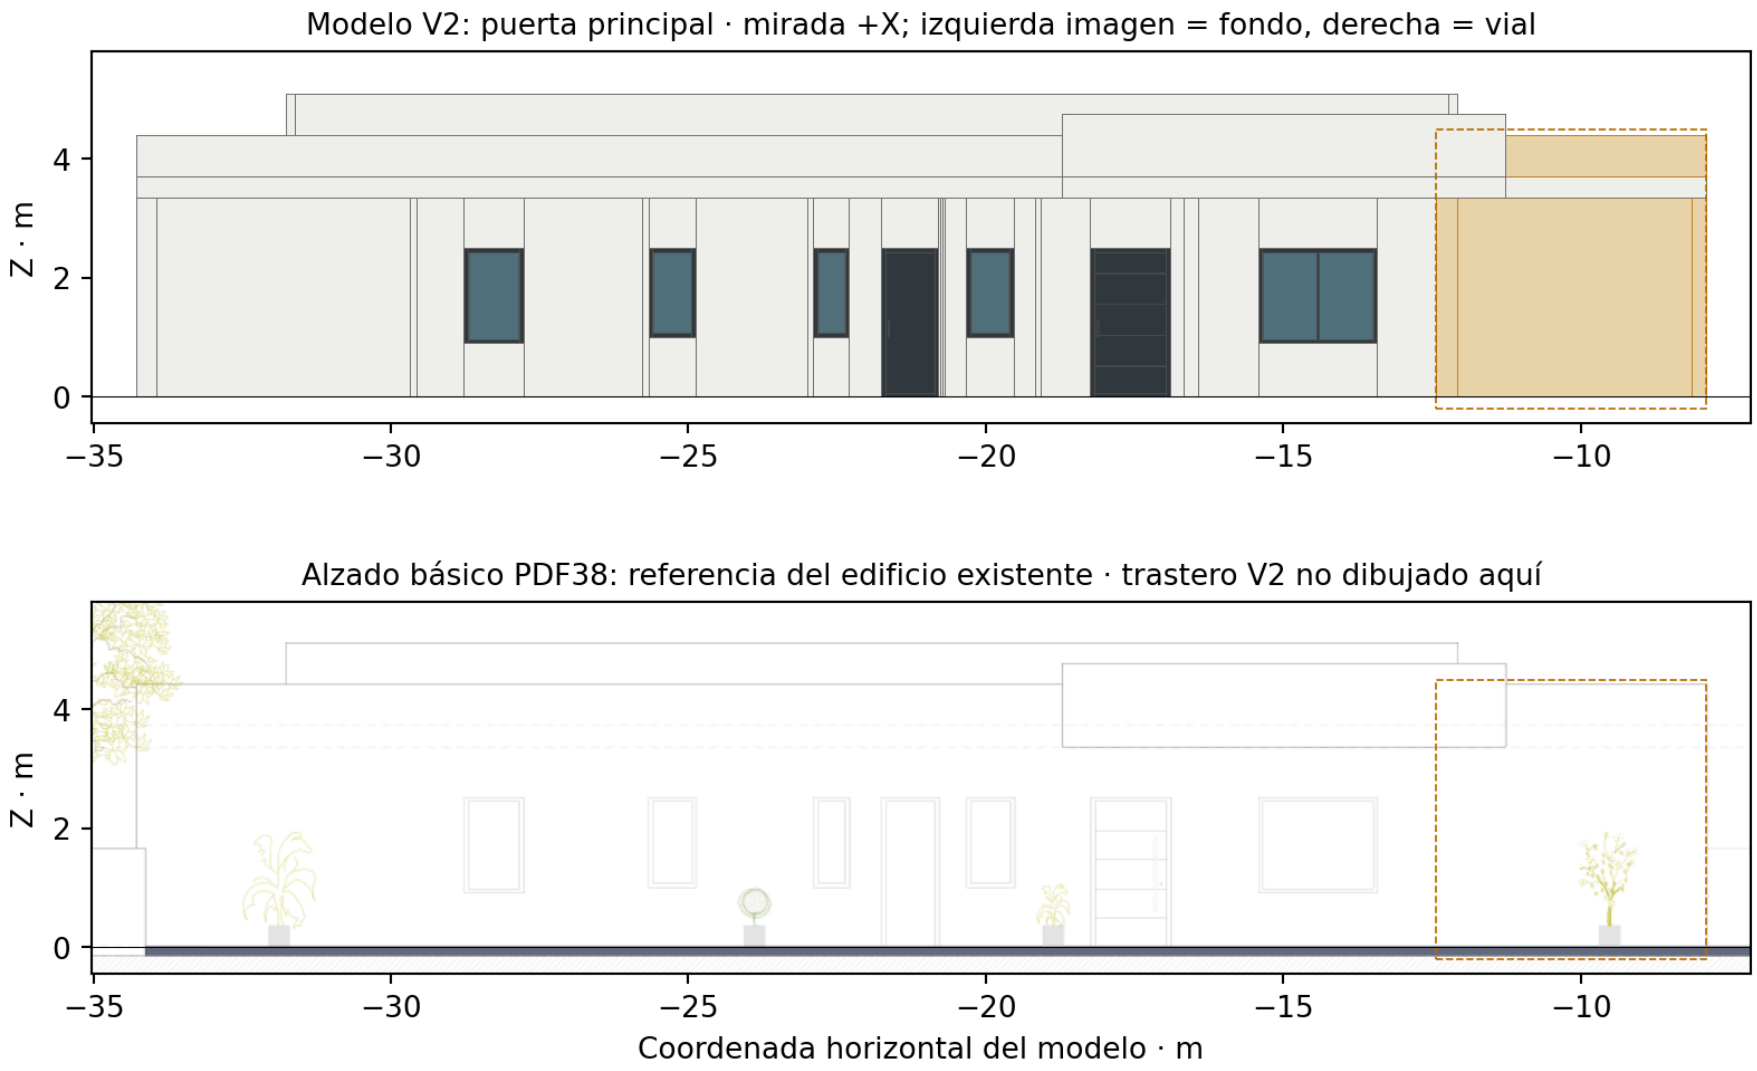

Banda ocre: ámbito del trastero añadido. Sus Z 3,35/3,70/4,40 y huecos 2,03/2,50 proceden del usuario.
El PDF definitivo sólo aporta XY. El cotejo no exige coincidir con la pérgola antigua del alzado básico.


Alzado · lateral porche

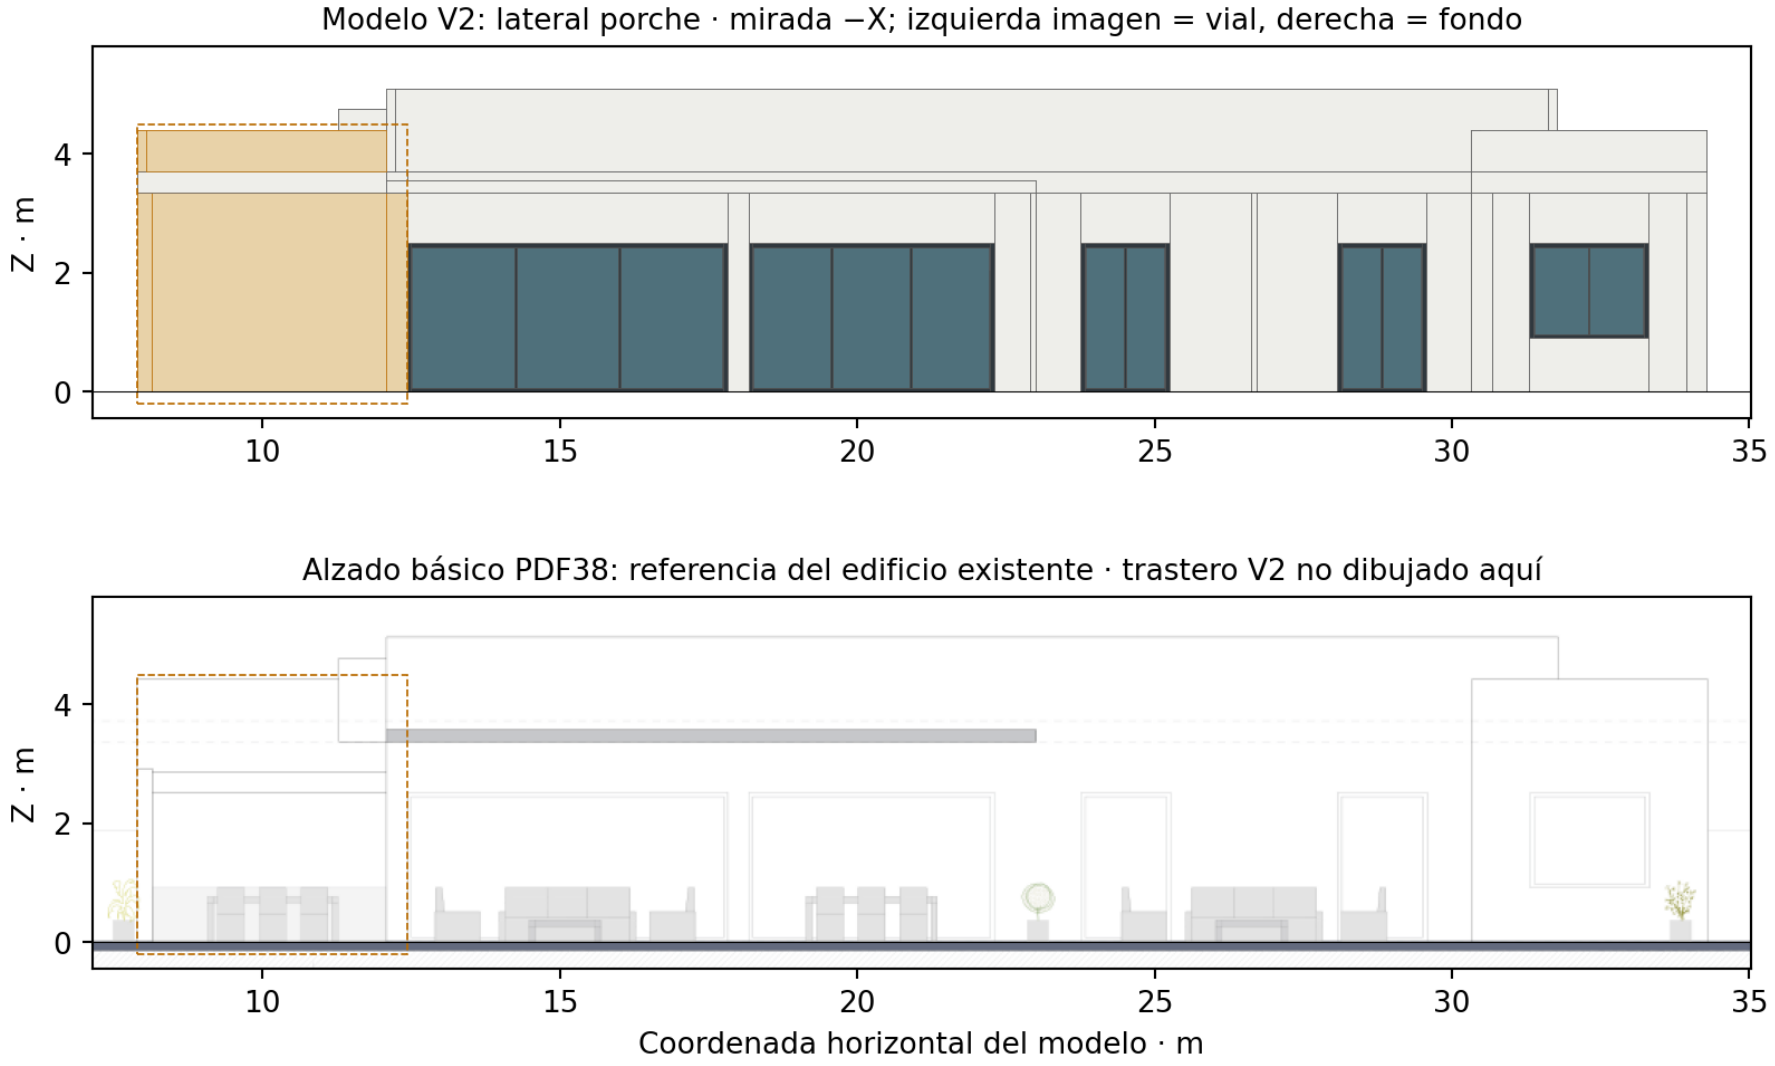


Banda ocre: ámbito del trastero añadido. Sus Z 3,35/3,70/4,40 y huecos 2,03/2,50 proceden del usuario.
El PDF definitivo sólo aporta XY. El cotejo no exige coincidir con la pérgola antigua del alzado básico.

Alzado · vial publico

Modelo V2: vial publico · mirada +Y; izquierda imagen = calle privada lateral

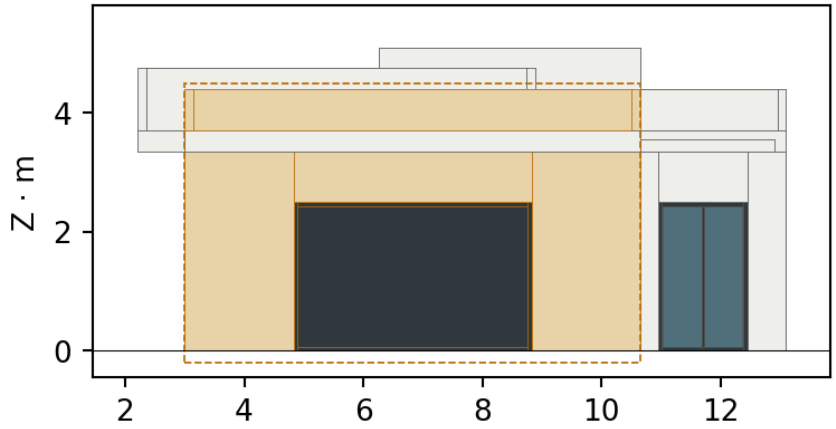


Alzado básico PDF38: referencia del edificio existente · trastero V2 no dibujado aquí

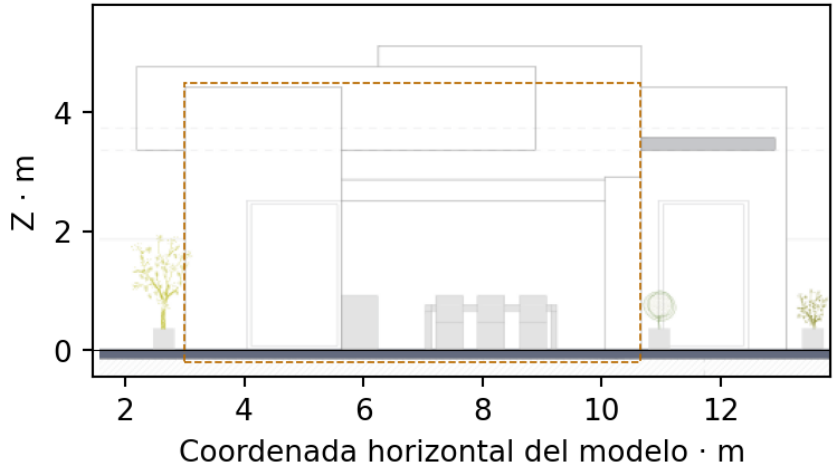


Banda ocre: ámbito del trastero añadido. Sus Z 3,35/3,70/4,40 y huecos 2,03/2,50 proceden del usuario.
El PDF definitivo sólo aporta XY. El cotejo no exige coincidir con la pérgola antigua del alzado básico.

Alzado · trasero

Modelo V2: trasero · mirada −Y; izquierda imagen = jardín lateral de terraza

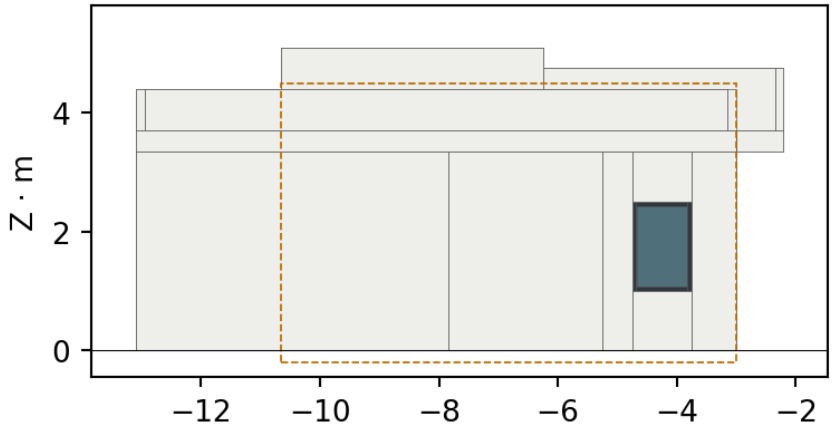


Alzado básico PDF38: referencia del edificio existente · trastero V2 no dibujado aquí

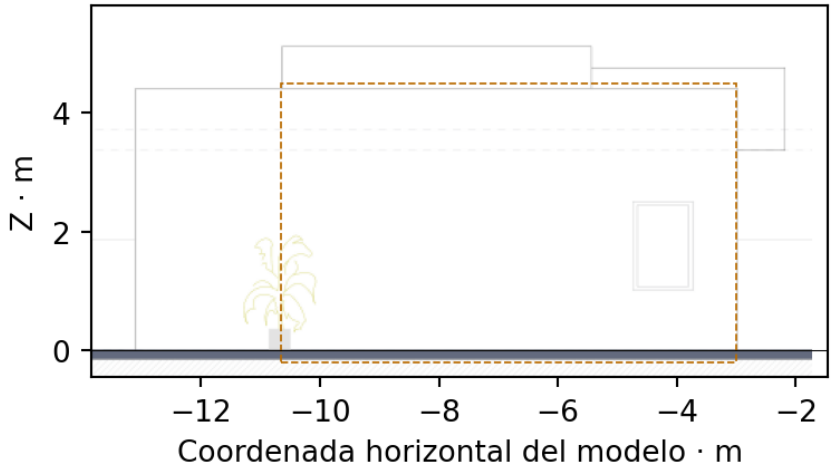

Banda ocre: ámbito del trastero añadido. Sus Z 3,35/3,70/4,40 y huecos 2,03/2,50 proceden del usuario.
El PDF definitivo sólo aporta XY. El cotejo no exige coincidir con la pérgola antigua del alzado básico.

Niveles del modelo y secciones originales

Cotas extraídas de los meshes V2
× negro modelo · azul básico · ocre usuario V2

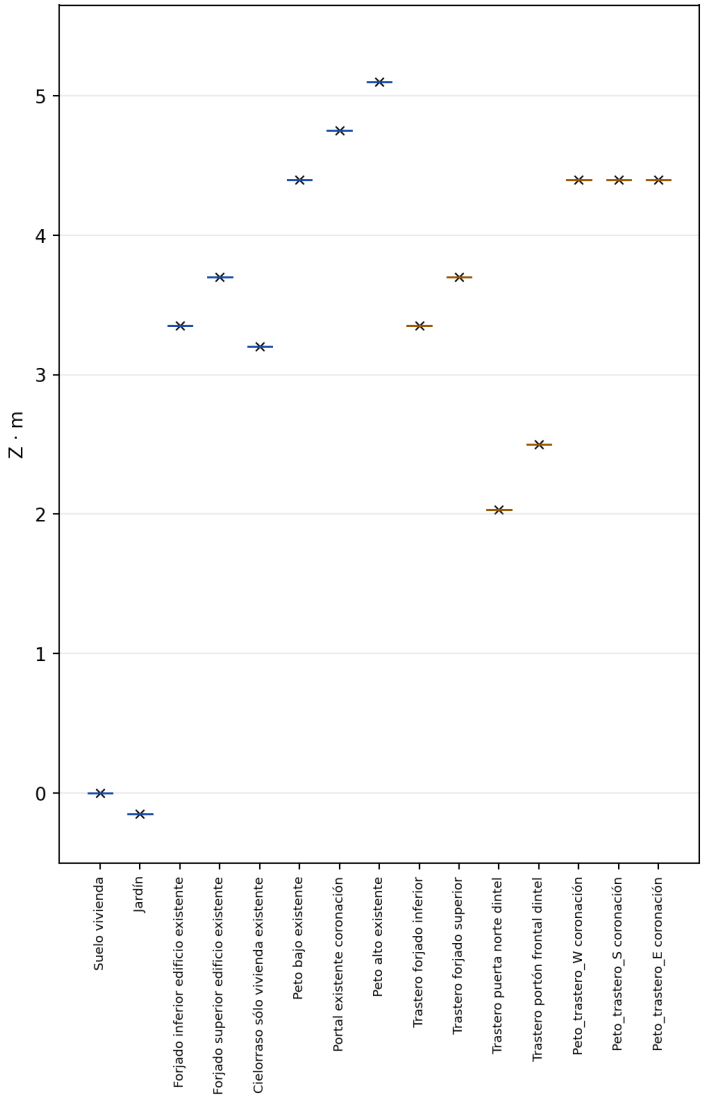


Secciones originales PDF39
Referencia de la geometría existente; no muestran el trastero definitivo



Comparación de niveles, no sección constructiva inventada. No se documenta un cielorraso nuevo del trastero.
La discrepancia de ancho del paño alto entre planta y trasero/sección3 permanece identificada en el control numérico.


Vista ortográfica V2 · PLANTA_CORTE

Fuente: mismo .blend y mismas mediciones que este informe. Vista analítica de control

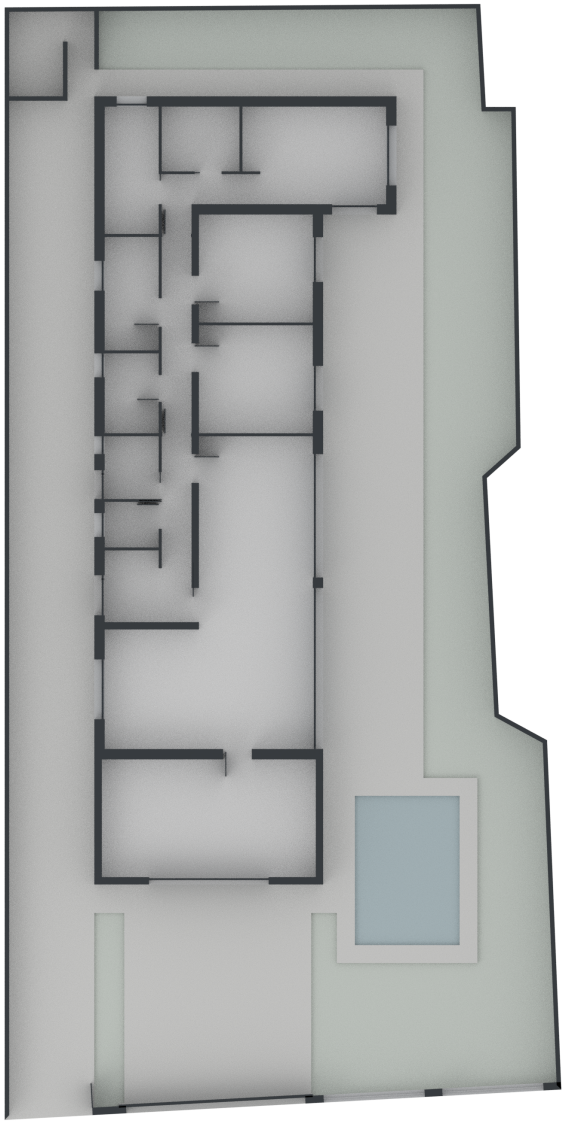


Vista ortográfica V2 · PLANTA_CUBIERTA

Fuente: mismo .blend y mismas mediciones que este informe. Vista analítica de control

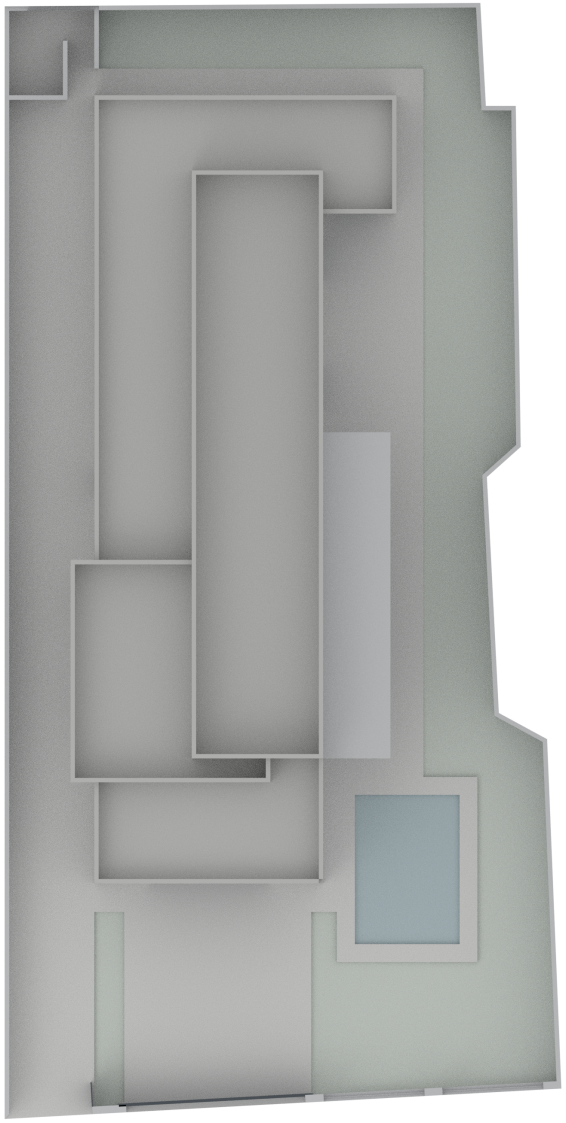

Vista ortográfica V2 · QA01

Fuente: mismo .blend y mismas mediciones que este informe. Vista analítica de control

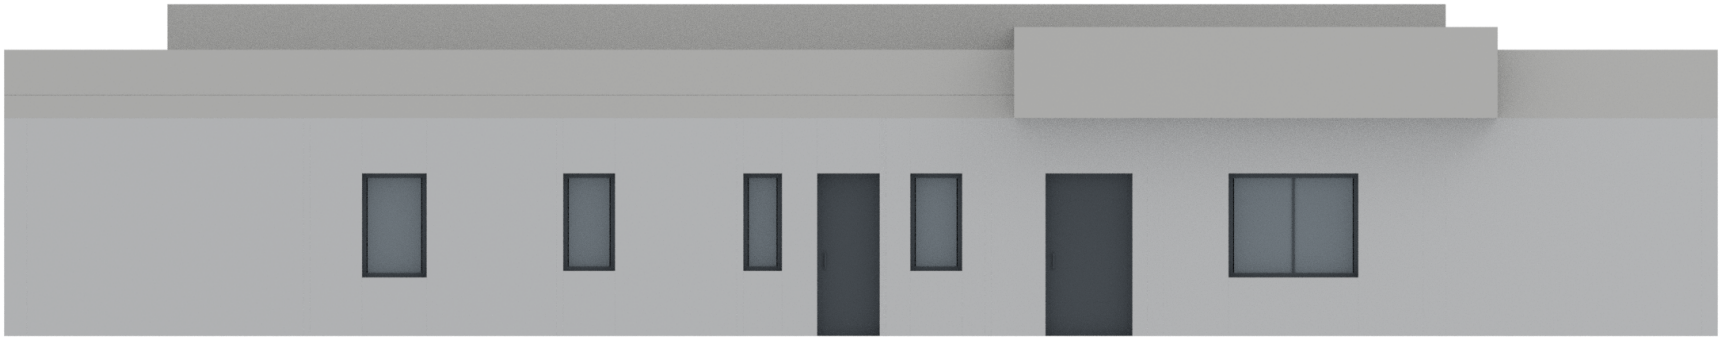

Vista ortográfica V2 · QA02

Fuente: mismo .blend y mismas mediciones que este informe. Vista analítica de control



Vista ortográfica V2 · QA03

Fuente: mismo .blend y mismas mediciones que este informe. Vista analítica de control



Vista ortográfica V2 · QA04

Fuente: mismo .blend y mismas mediciones que este informe. Vista analítica de control



Geometría principal · valores medidos

Elemento	Modelo	Referencia	Diferencia	Obtención / fuente
Trastero ancho interior m	7.15000	7.15000	+0.000000	Cota directa · PDF final1
Trastero fondo interior m	3.94000	3.94000	-0.000000	Cota directa · PDF final1
Trastero fondo hasta exterior sur m	4.19000	4.19000	-0.000000	Cota directa · PDF final1
Trastero hueco norte ancho m	0.96000	0.96000	+0.000000	Cota directa · PDF final1
Trastero portón sur ancho m	4.00050	4.00050	-0.000000	Calculada del vector · PDF final1
Trastero superficie interior más umbral m²	29.17112	29.17000	+0.001123	Deducción del cómputo; no forzar perímetro · Etiqueta PDF final1
Piscina ancho XY m	3.50000	3.50000	+0.000000	Cota directa · PDF final1
Piscina largo XY m	5.00000	5.00000	-0.000000	Cota directa · PDF final1
Piscina superficie XY m²	17.50000	17.50000	-0.000002	Cotas directas · PDF final1
Parcela área del trazo m²	635.73859	635.60000	+0.138594	Vector del lindero; área rotulada no fuerza contorno · Básico memoria / PDF final1
V_bano1_norte ancho de hueco m	1.00330	—	—	Mesh medido; comparar con tabla numérica V2 · PDF38 alzados; medidas gráficas calculadas, nominales contrastadas con memoria19/20.
V_despacho_oeste ancho de hueco m	0.99695	—	—	Mesh medido; comparar con tabla numérica V2 · PDF38 alzados; medidas gráficas calculadas, nominales contrastadas con memoria19/20.
V_bano2_oeste ancho de hueco m	0.80010	—	—	Mesh medido; comparar con tabla numérica V2 · PDF38 alzados; medidas gráficas calculadas, nominales contrastadas con memoria19/20.
V_lavadero_oeste ancho de hueco m	0.59690	—	—	Mesh medido; comparar con tabla numérica V2 · PDF38 alzados; medidas gráficas calculadas, nominales contrastadas con memoria19/20.
P_lavadero_oeste ancho de hueco m	0.96520	—	—	Mesh medido; comparar con tabla numérica V2 · PDF38 alzados; medidas gráficas calculadas, nominales contrastadas con memoria19/20.
V_aseo_oeste ancho de hueco m	0.80010	—	—	Mesh medido; comparar con tabla numérica V2 · PDF38 alzados; medidas gráficas calculadas, nominales contrastadas con memoria19/20.

Elemento	Modelo	Referencia	Diferencia	Obtención / fuente
P_principal_oeste ancho de hueco m	1.33985	—	—	Mesh medido; comparar con tabla numérica V2 · PDF38 alzados; medidas gráficas calculadas, nominales contrastadas con memoria19/20.
V_salon_oeste ancho de hueco m	2.00025	—	—	Mesh medido; comparar con tabla numérica V2 · PDF38 alzados; medidas gráficas calculadas, nominales contrastadas con memoria19/20.
V_dormitorio1_este ancho de hueco m	2.00025	—	—	Mesh medido; comparar con tabla numérica V2 · PDF38 alzados; medidas gráficas calculadas, nominales contrastadas con memoria19/20.
V_dormitorio1_sur ancho de hueco m	1.49860	—	—	Mesh medido; comparar con tabla numérica V2 · PDF38 alzados; medidas gráficas calculadas, nominales contrastadas con memoria19/20.
V_dormitorio2_este ancho de hueco m	1.49860	—	—	Mesh medido; comparar con tabla numérica V2 · PDF38 alzados; medidas gráficas calculadas, nominales contrastadas con memoria19/20.
V_dormitorio3_este ancho de hueco m	1.49860	—	—	Mesh medido; comparar con tabla numérica V2 · PDF38 alzados; medidas gráficas calculadas, nominales contrastadas con memoria19/20.
V_cocina_este ancho de hueco m	4.13385	—	—	Mesh medido; comparar con tabla numérica V2 · PDF38 alzados; medidas gráficas calculadas, nominales contrastadas con memoria19/20.
V_salon_este ancho de hueco m	5.39115	—	—	Mesh medido; comparar con tabla numérica V2 · PDF38 alzados; medidas gráficas calculadas, nominales contrastadas con memoria19/20.

Niveles · origen de las referencias

Elemento	Z modelo	Z referencia	Diferencia	Origen
Suelo vivienda	0.00000	0.00	+0.000000	Básico · Datum PDF38/39
Jardín	-0.15000	-0.15	-0.000000	Básico · PDF38/39
Forjado inferior edificio existente	3.35000	3.35	-0.000000	Básico · PDF38/39
Forjado superior edificio existente	3.70000	3.70	+0.000000	Básico · PDF38/39
Cielorraso sólo vivienda existente	3.20000	3.20	+0.000000	Calculada del básico · Secciones1/3; no se aplica al trastero
Peto bajo existente	4.40000	4.40	+0.000000	Básico · PDF38/39
Portal existente coronación	4.75000	4.75	+0.000000	Básico · PDF38/39
Peto alto existente	5.10000	5.10	-0.000000	Básico · PDF38/39
Trastero forjado inferior	3.35000	3.35	-0.000000	Usuario V2 · Confirmación expresa del usuario; forjado continuo
Trastero forjado superior	3.70000	3.70	+0.000000	Usuario V2 · Confirmación expresa del usuario; forjado continuo
Trastero puerta norte dintel	2.03000	2.03	-0.000000	Usuario V2 · Confirmación expresa del usuario
Trastero portón frontal dintel	2.50000	2.50	+0.000000	Usuario V2 · Confirmación expresa del usuario
Peto_trastero_W coronación	4.40000	4.40	+0.000000	Usuario V2 · Confirmación expresa del usuario
Peto_trastero_S coronación	4.40000	4.40	+0.000000	Usuario V2 · Confirmación expresa del usuario
Peto_trastero_E coronación	4.40000	4.40	+0.000000	Usuario V2 · Confirmación expresa del usuario